


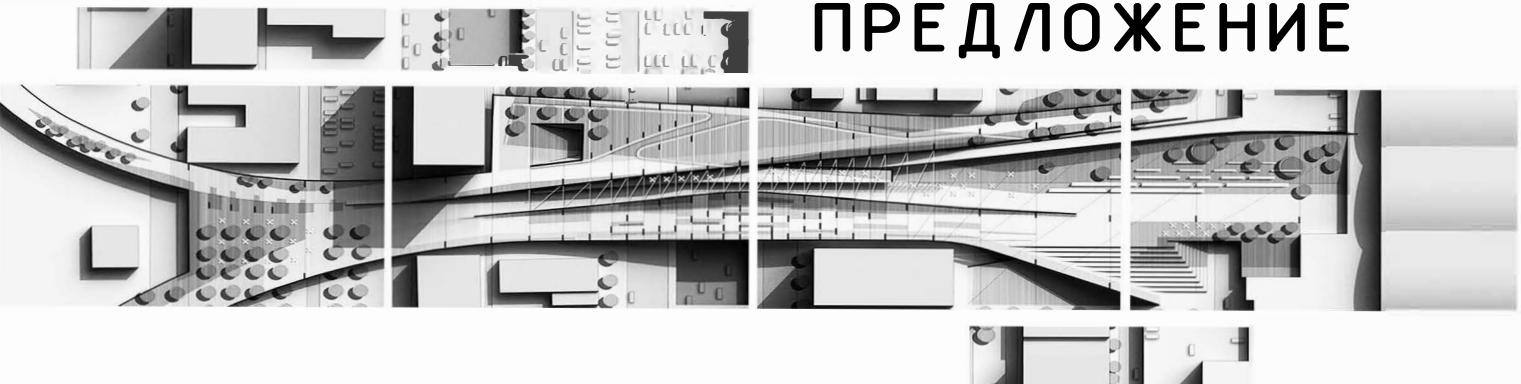

ПРОЕКТНОЕ ПРЕДЛОЖЕНИЕ




Проект 12-ти этажного комплекса
по адресу: г. Избербаш, Республика Дагестан.








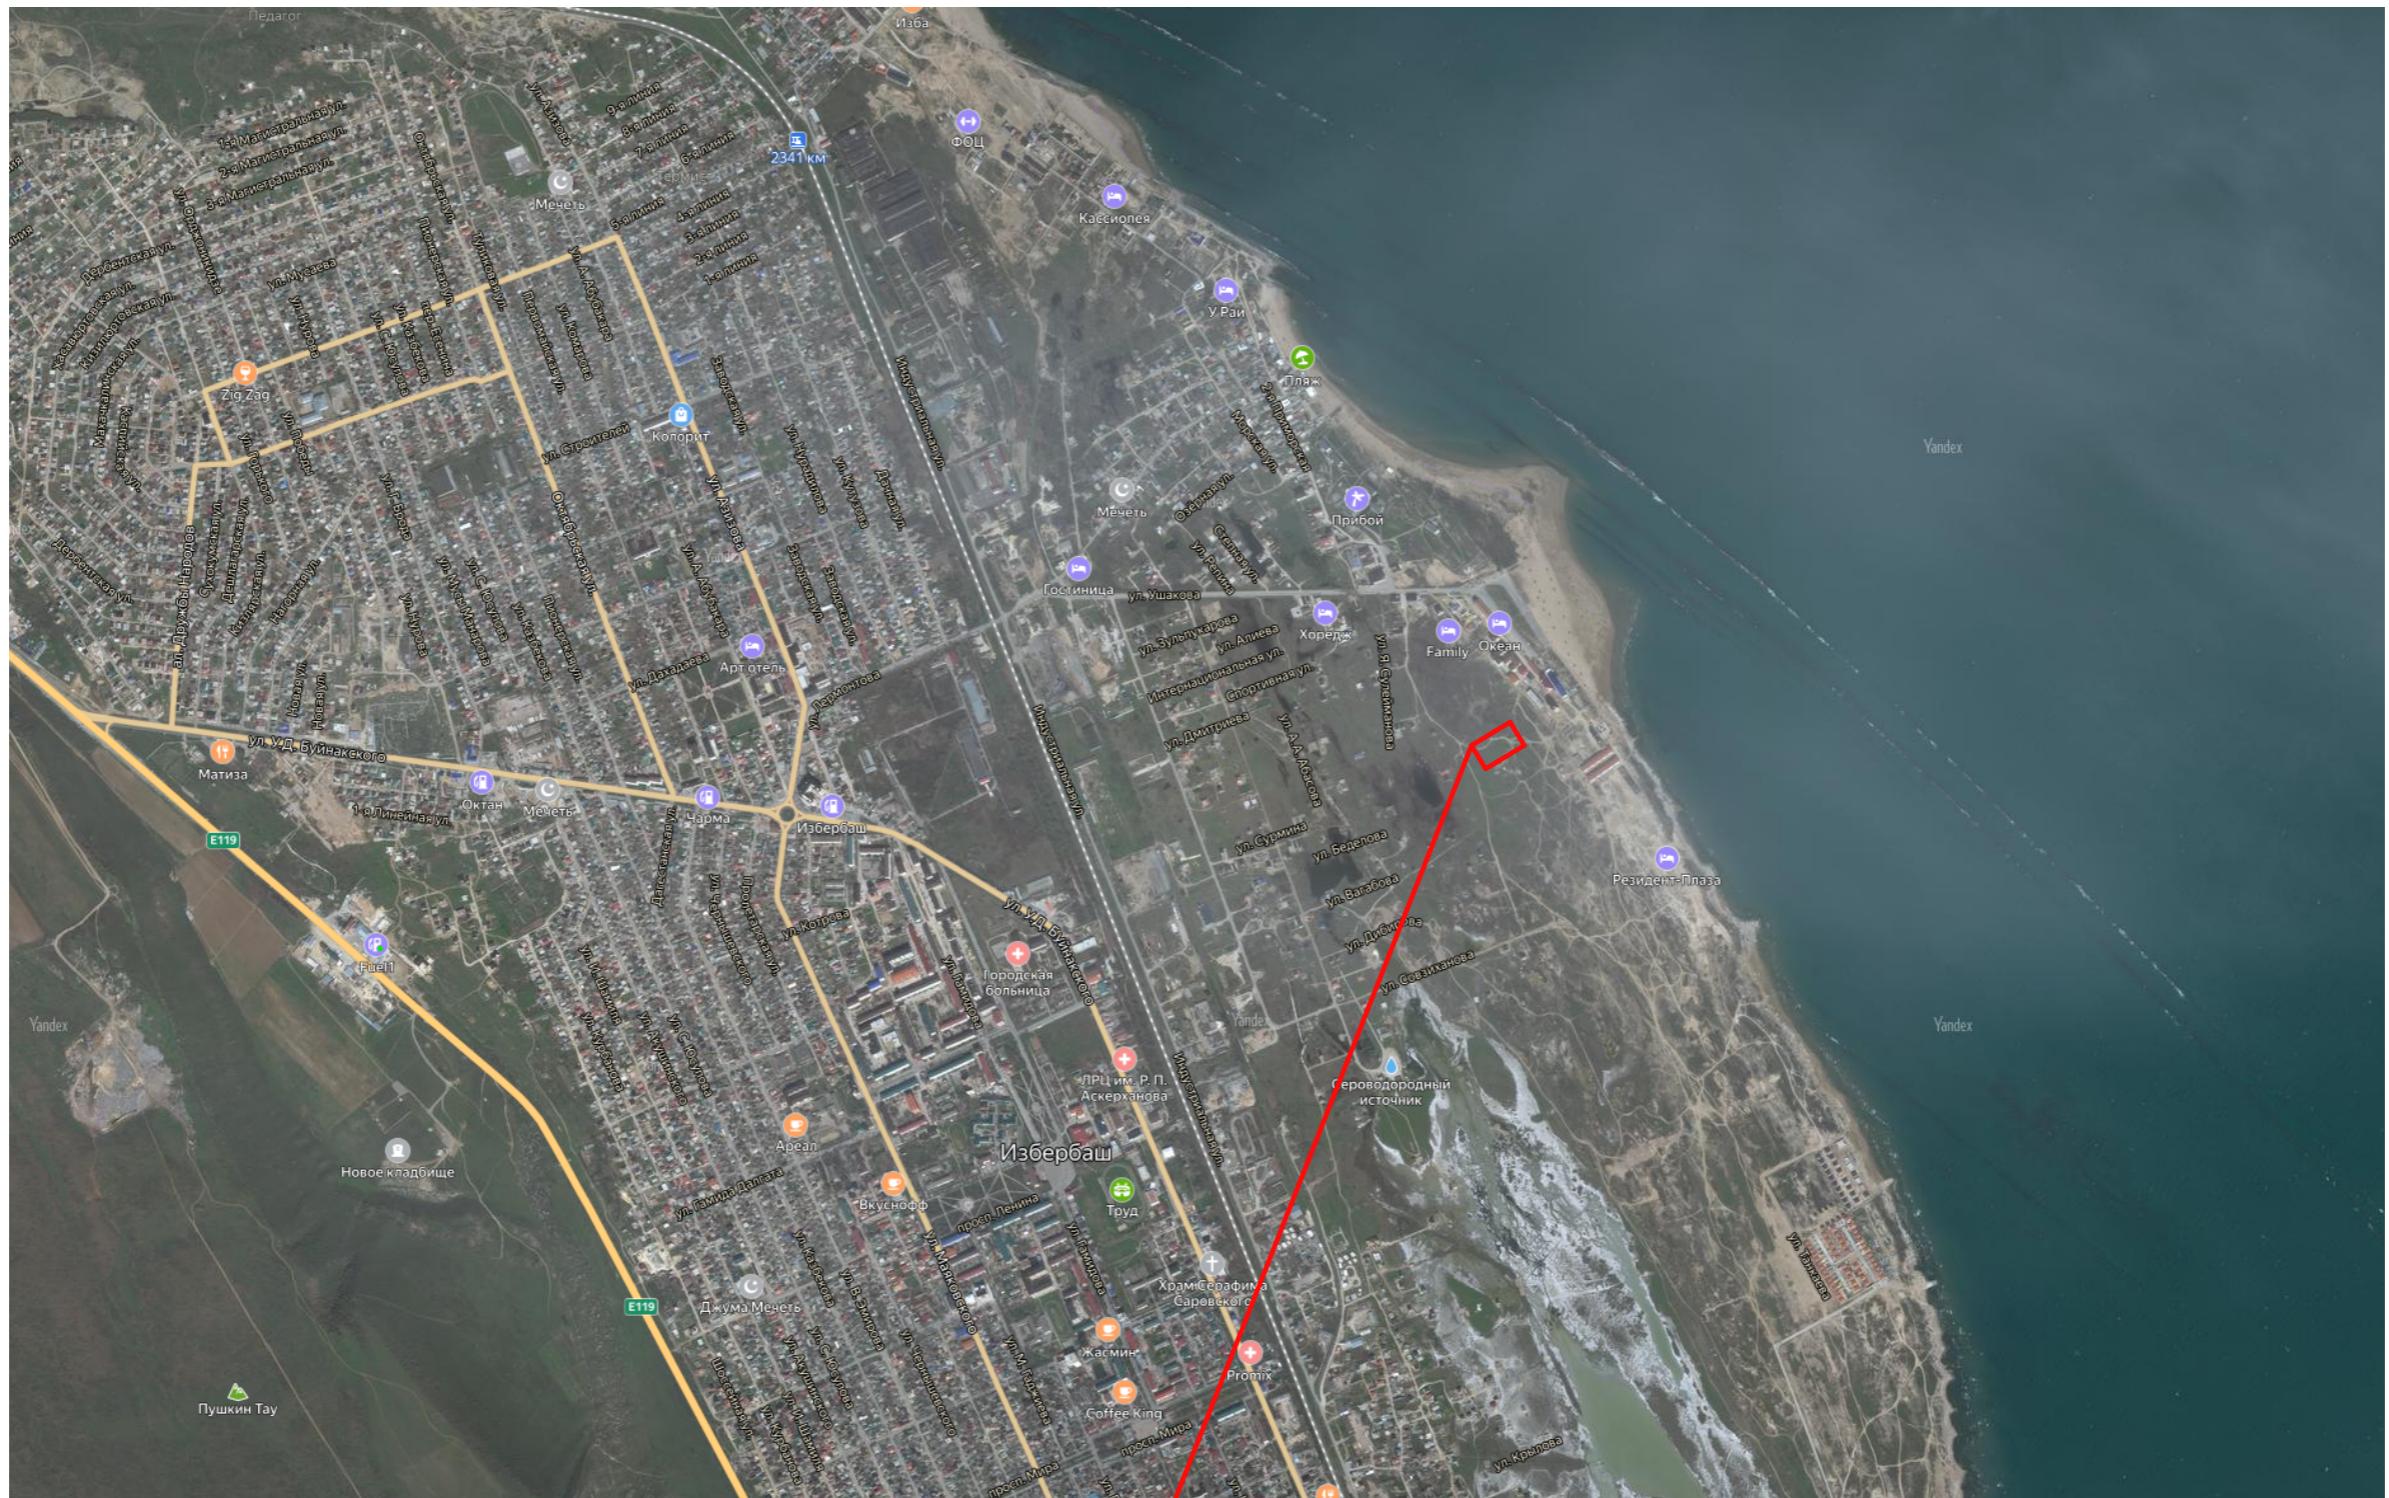


Участок строительства

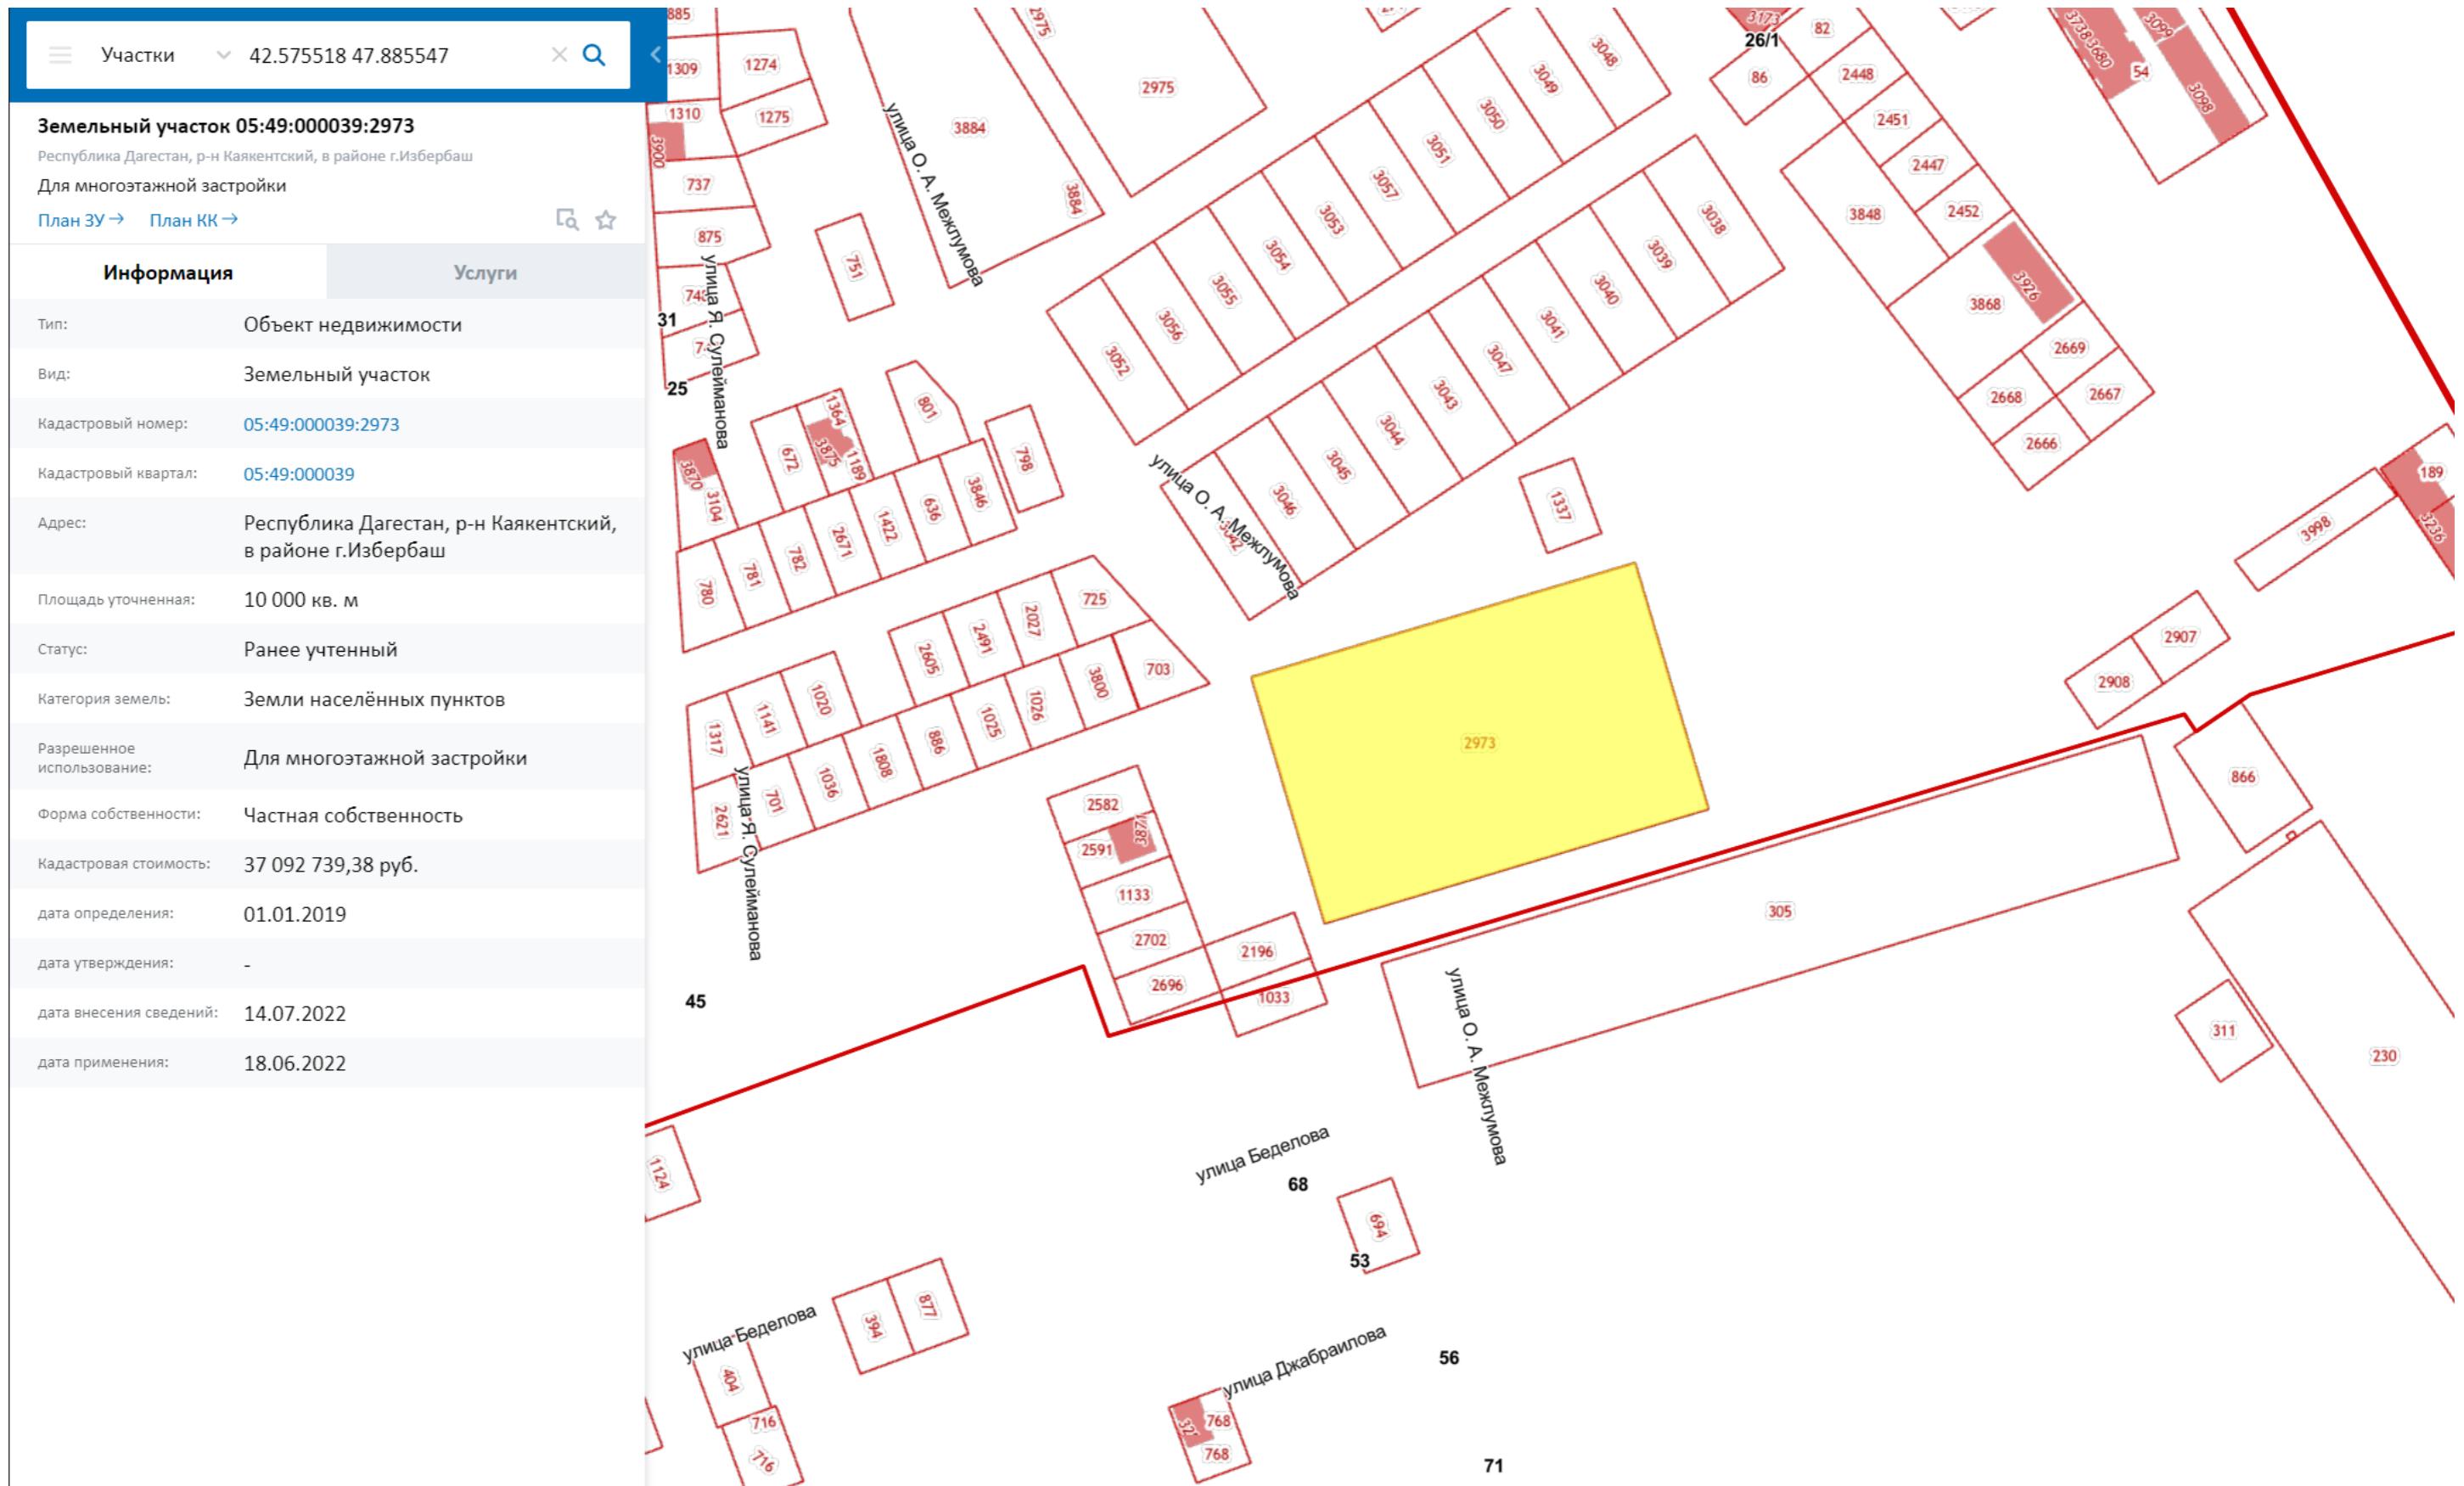

Генплан участка М 1:500

381700 ~~1733~~

381700 ~~1733~~

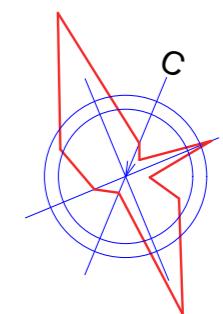


Условные обозначения


- Проектируемое здание
- Озеленение
- Тротуарная плитка
- Асфальтовое покрытие
- Детская площадка
- Существующая постройка
- Мусорные баки
- Граница участка

Технико-экономические показатели.

Наименование	Ед. изм.	Кол-во	%	Примеч.
1. Площадь участка	м ²	10 000	100	
2. Площадь застройки	м ²	4 950	49,5	
3. Количество квартир	штук	1 210		
4. Общая площадь квартир	м ²	48 444		
5. Площадь коммерции	м ²	4 042		
6. Площадь цокольного этажа	м ²	4 042		
7. Этажность	штук	12		
8. Площадь двора по СП 10% от участка	м ²	1 015	10,15	

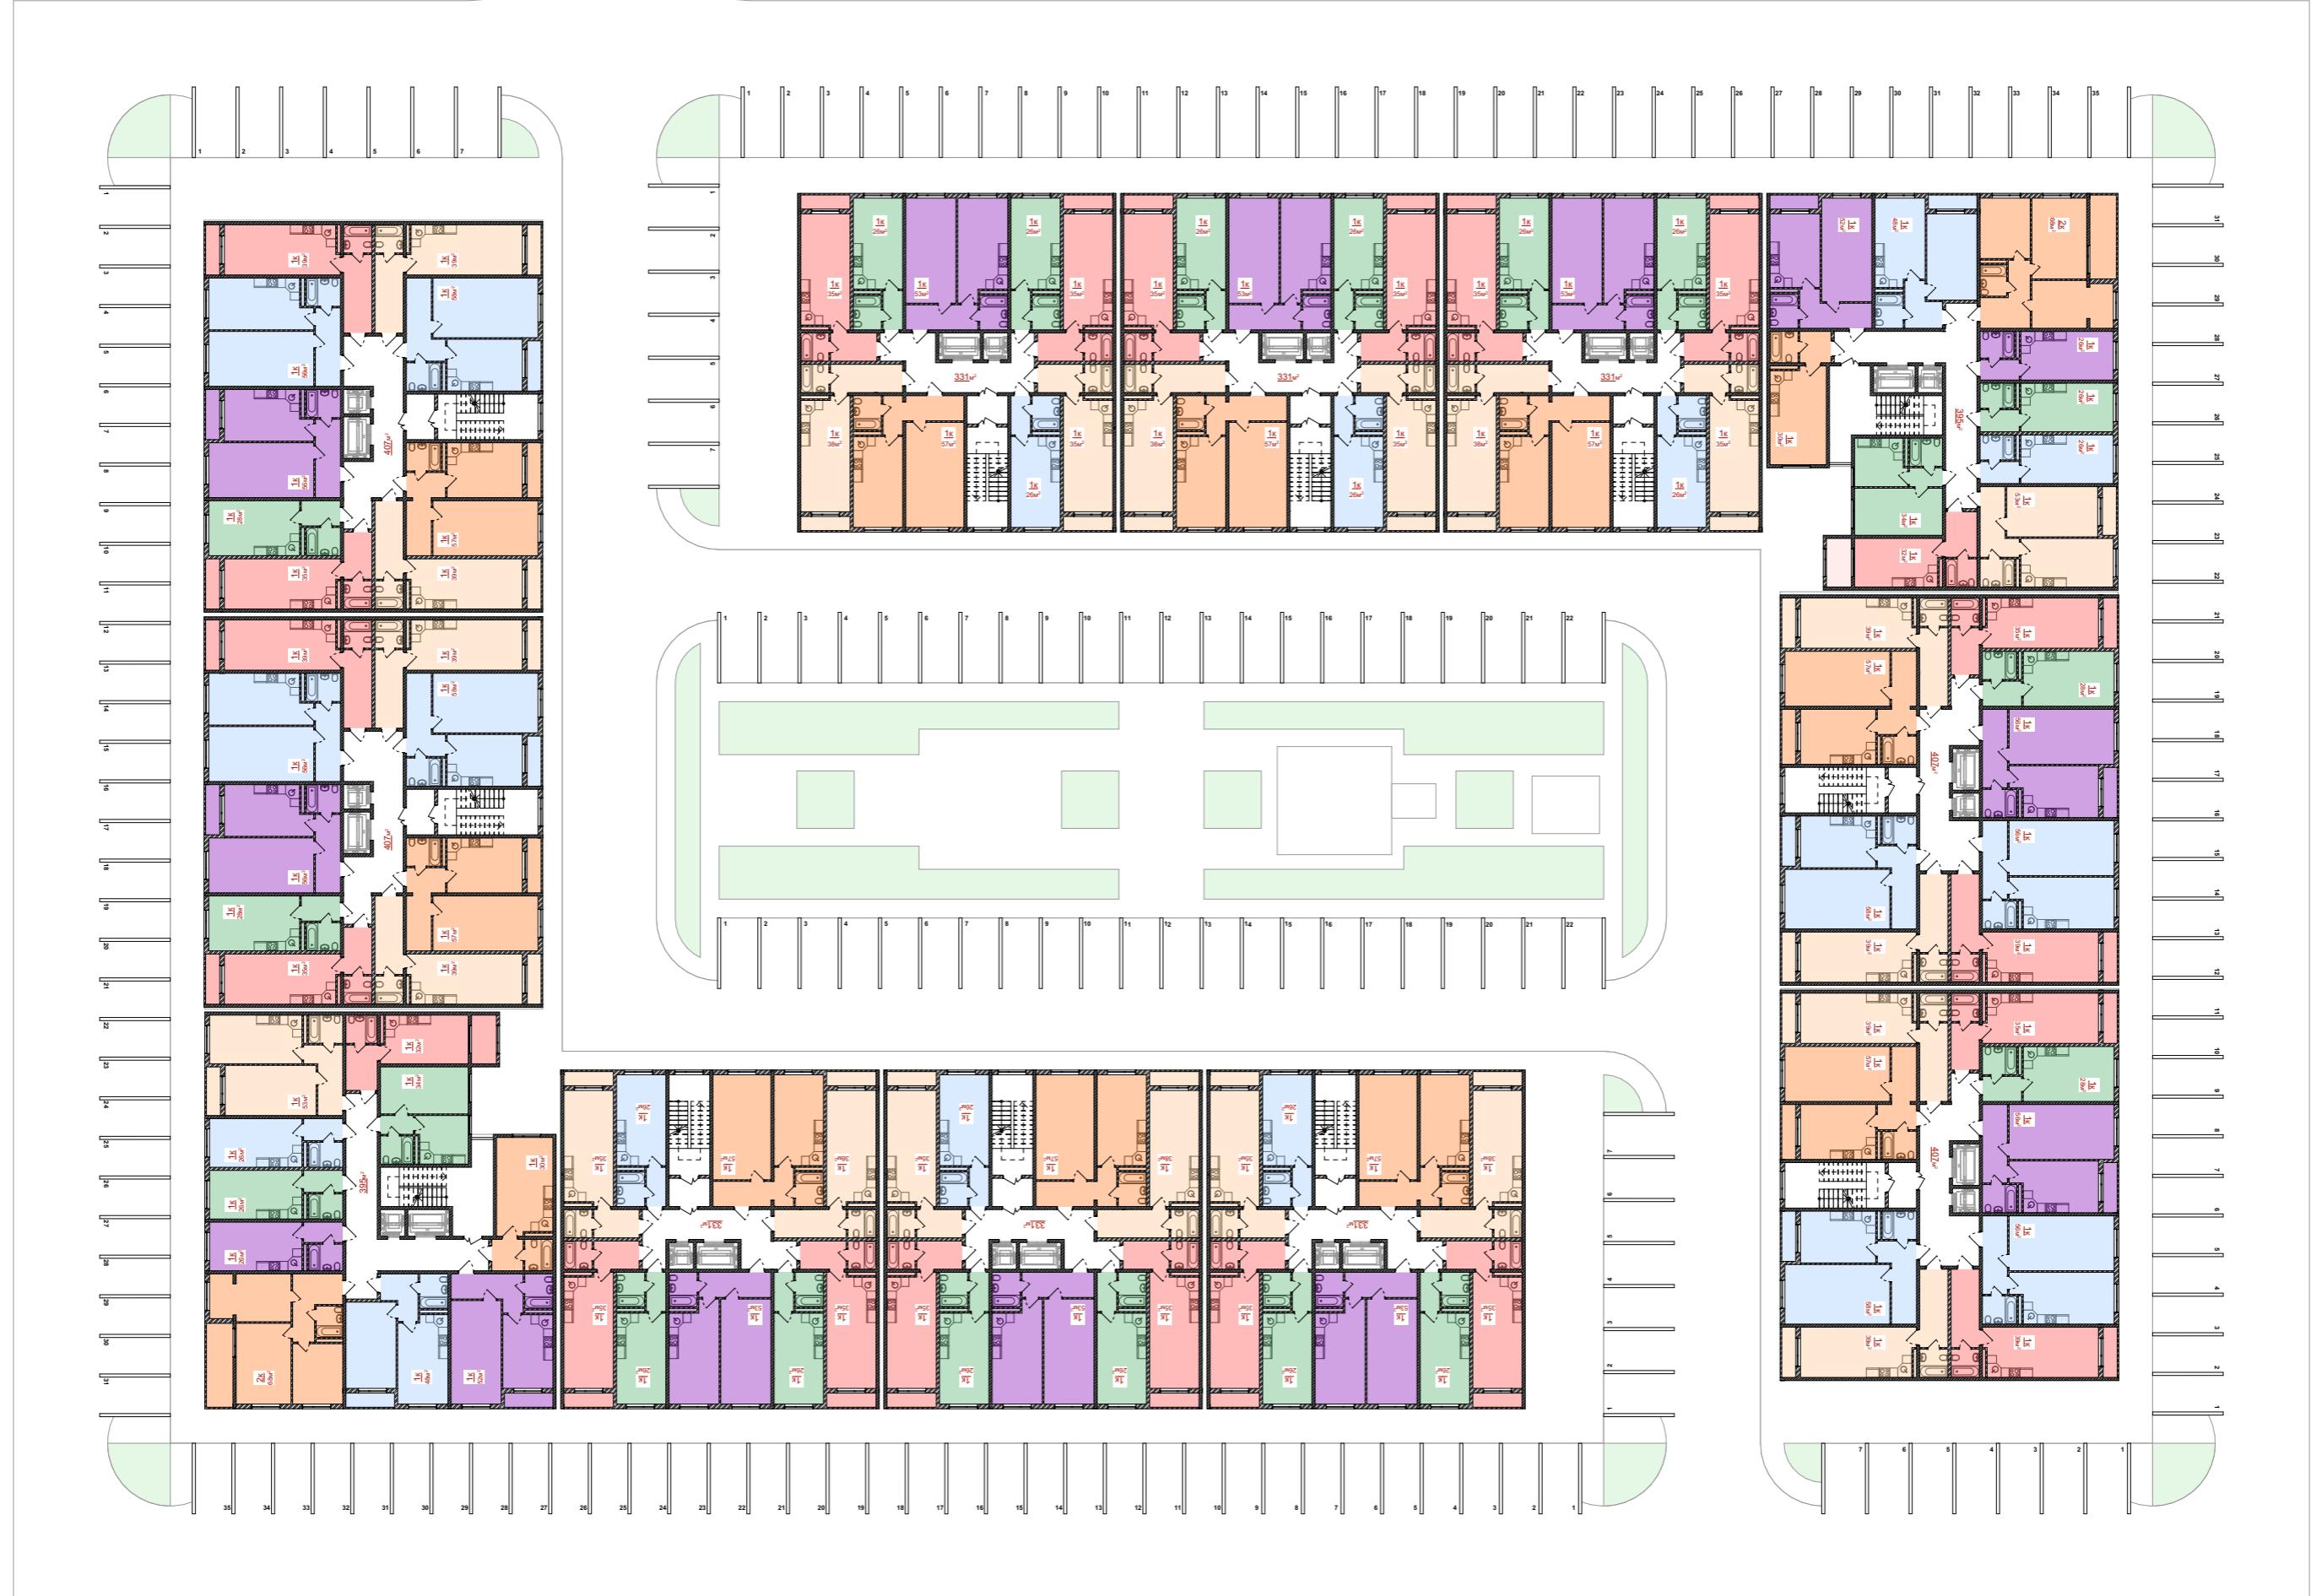


План 1 го этажа

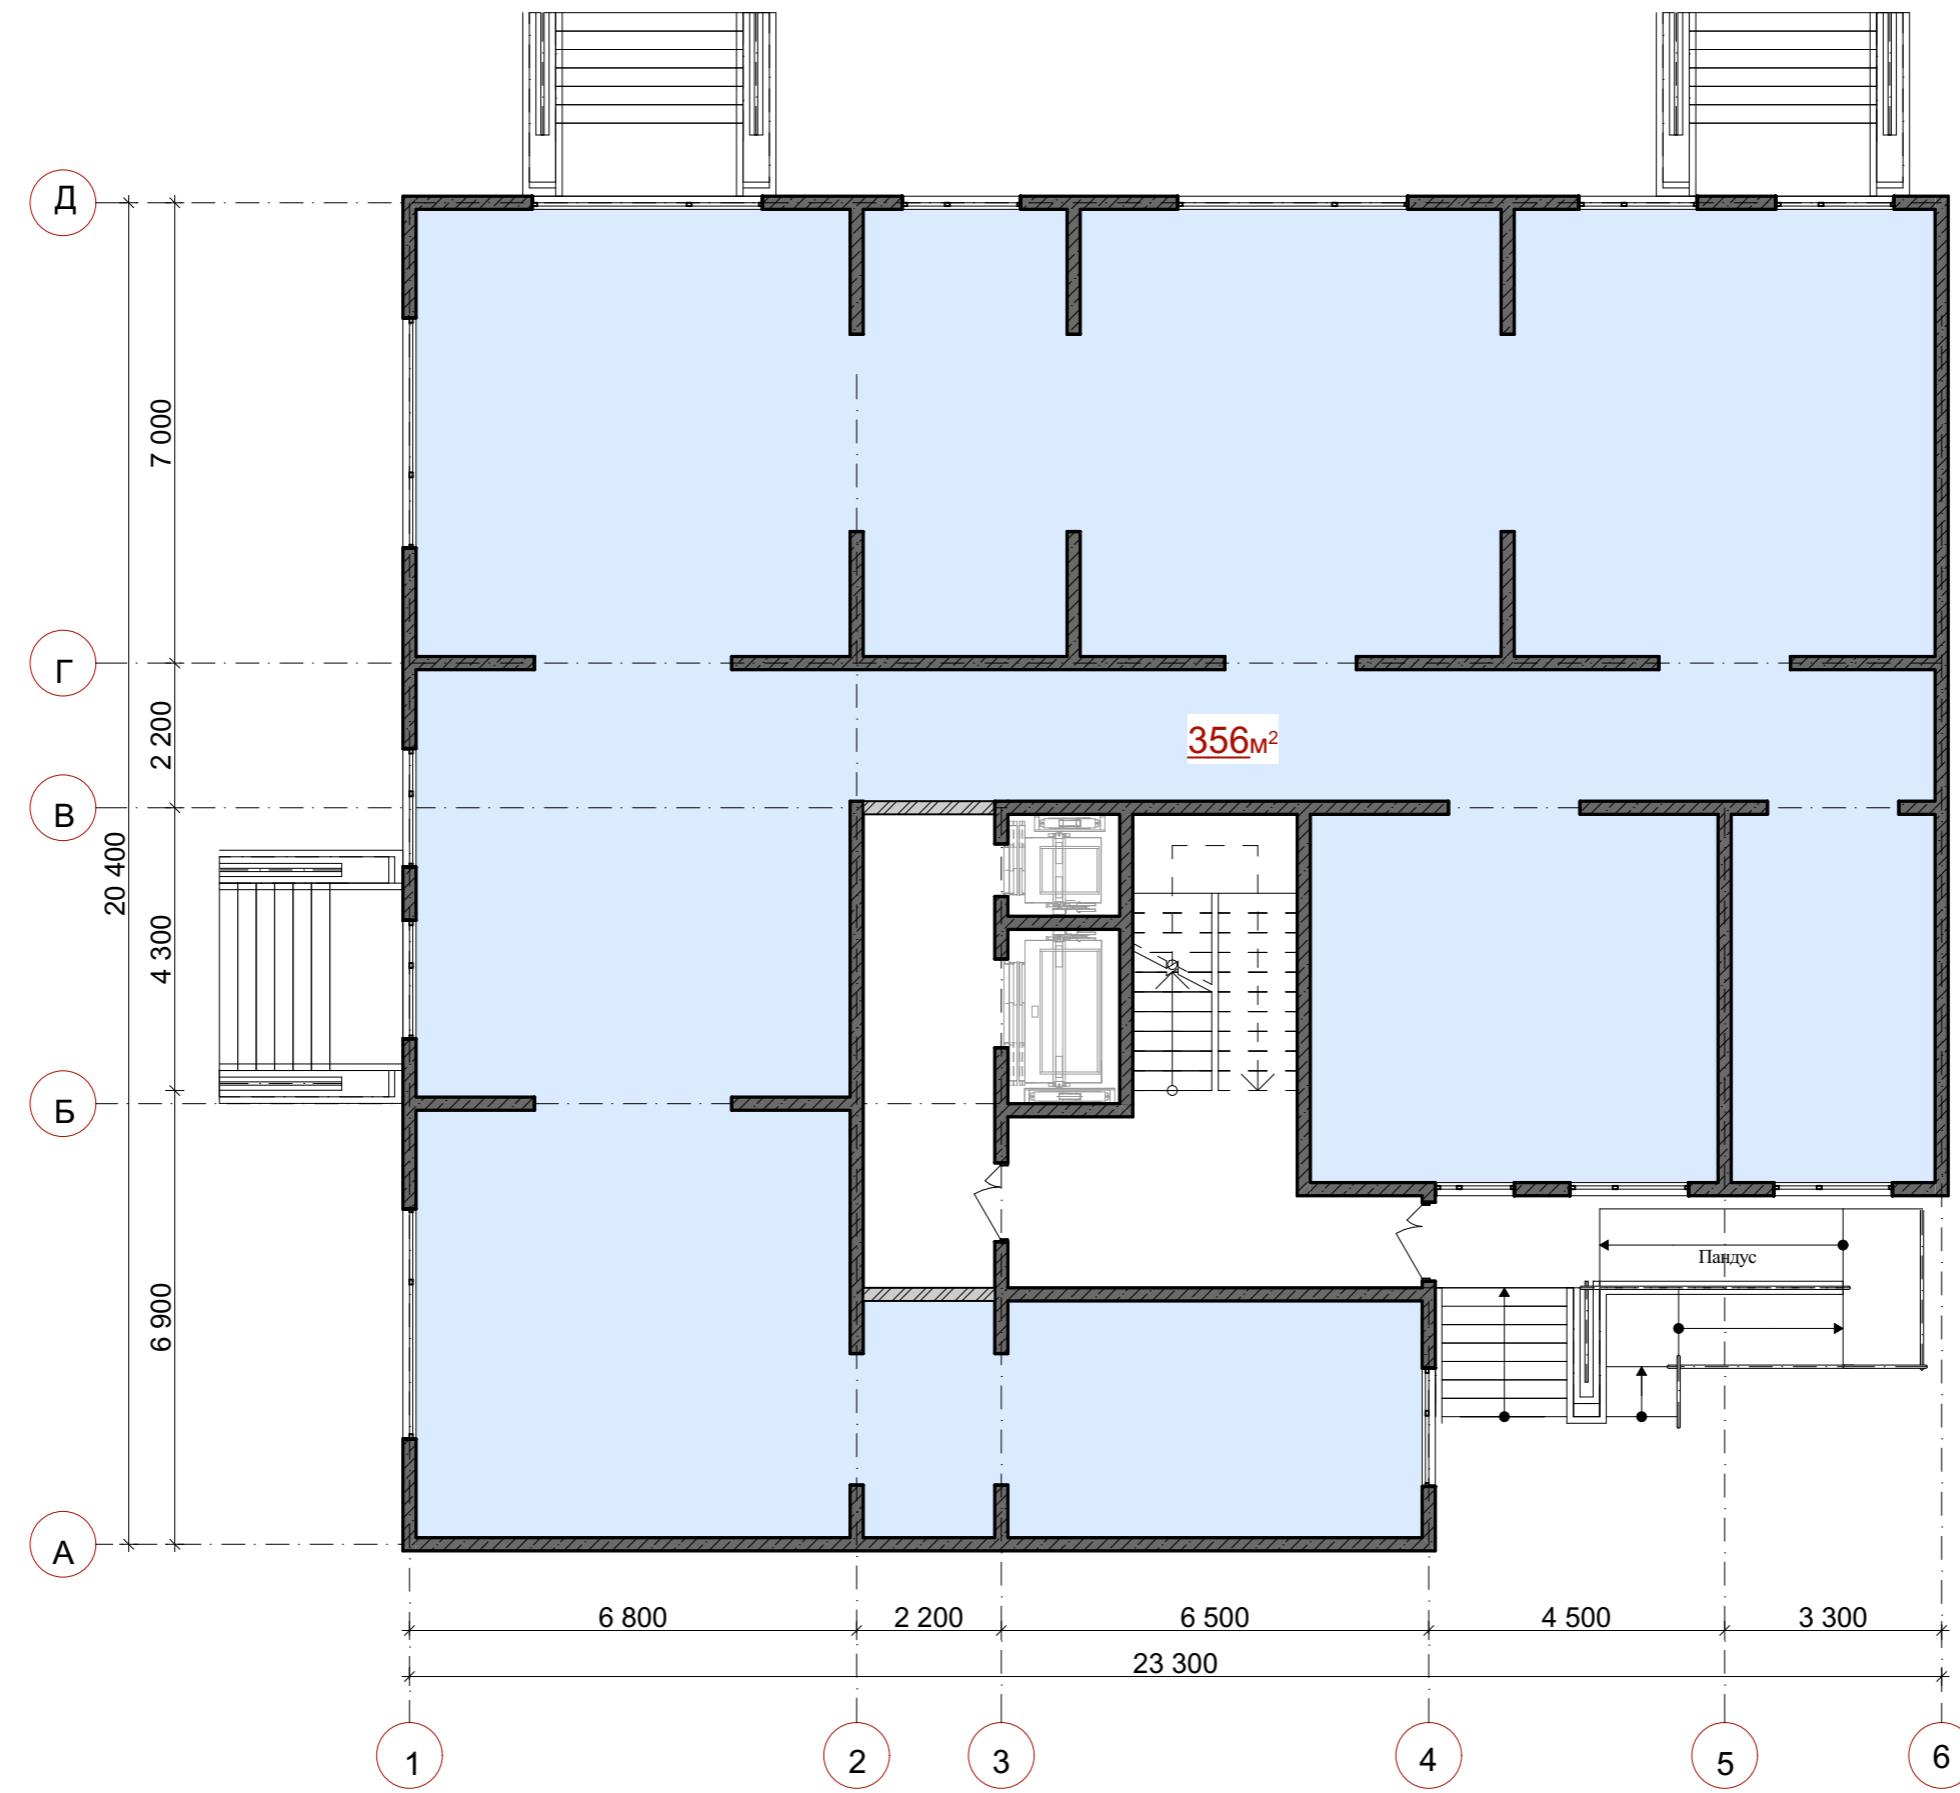

План 2-12 этажа




План 1 го этажа

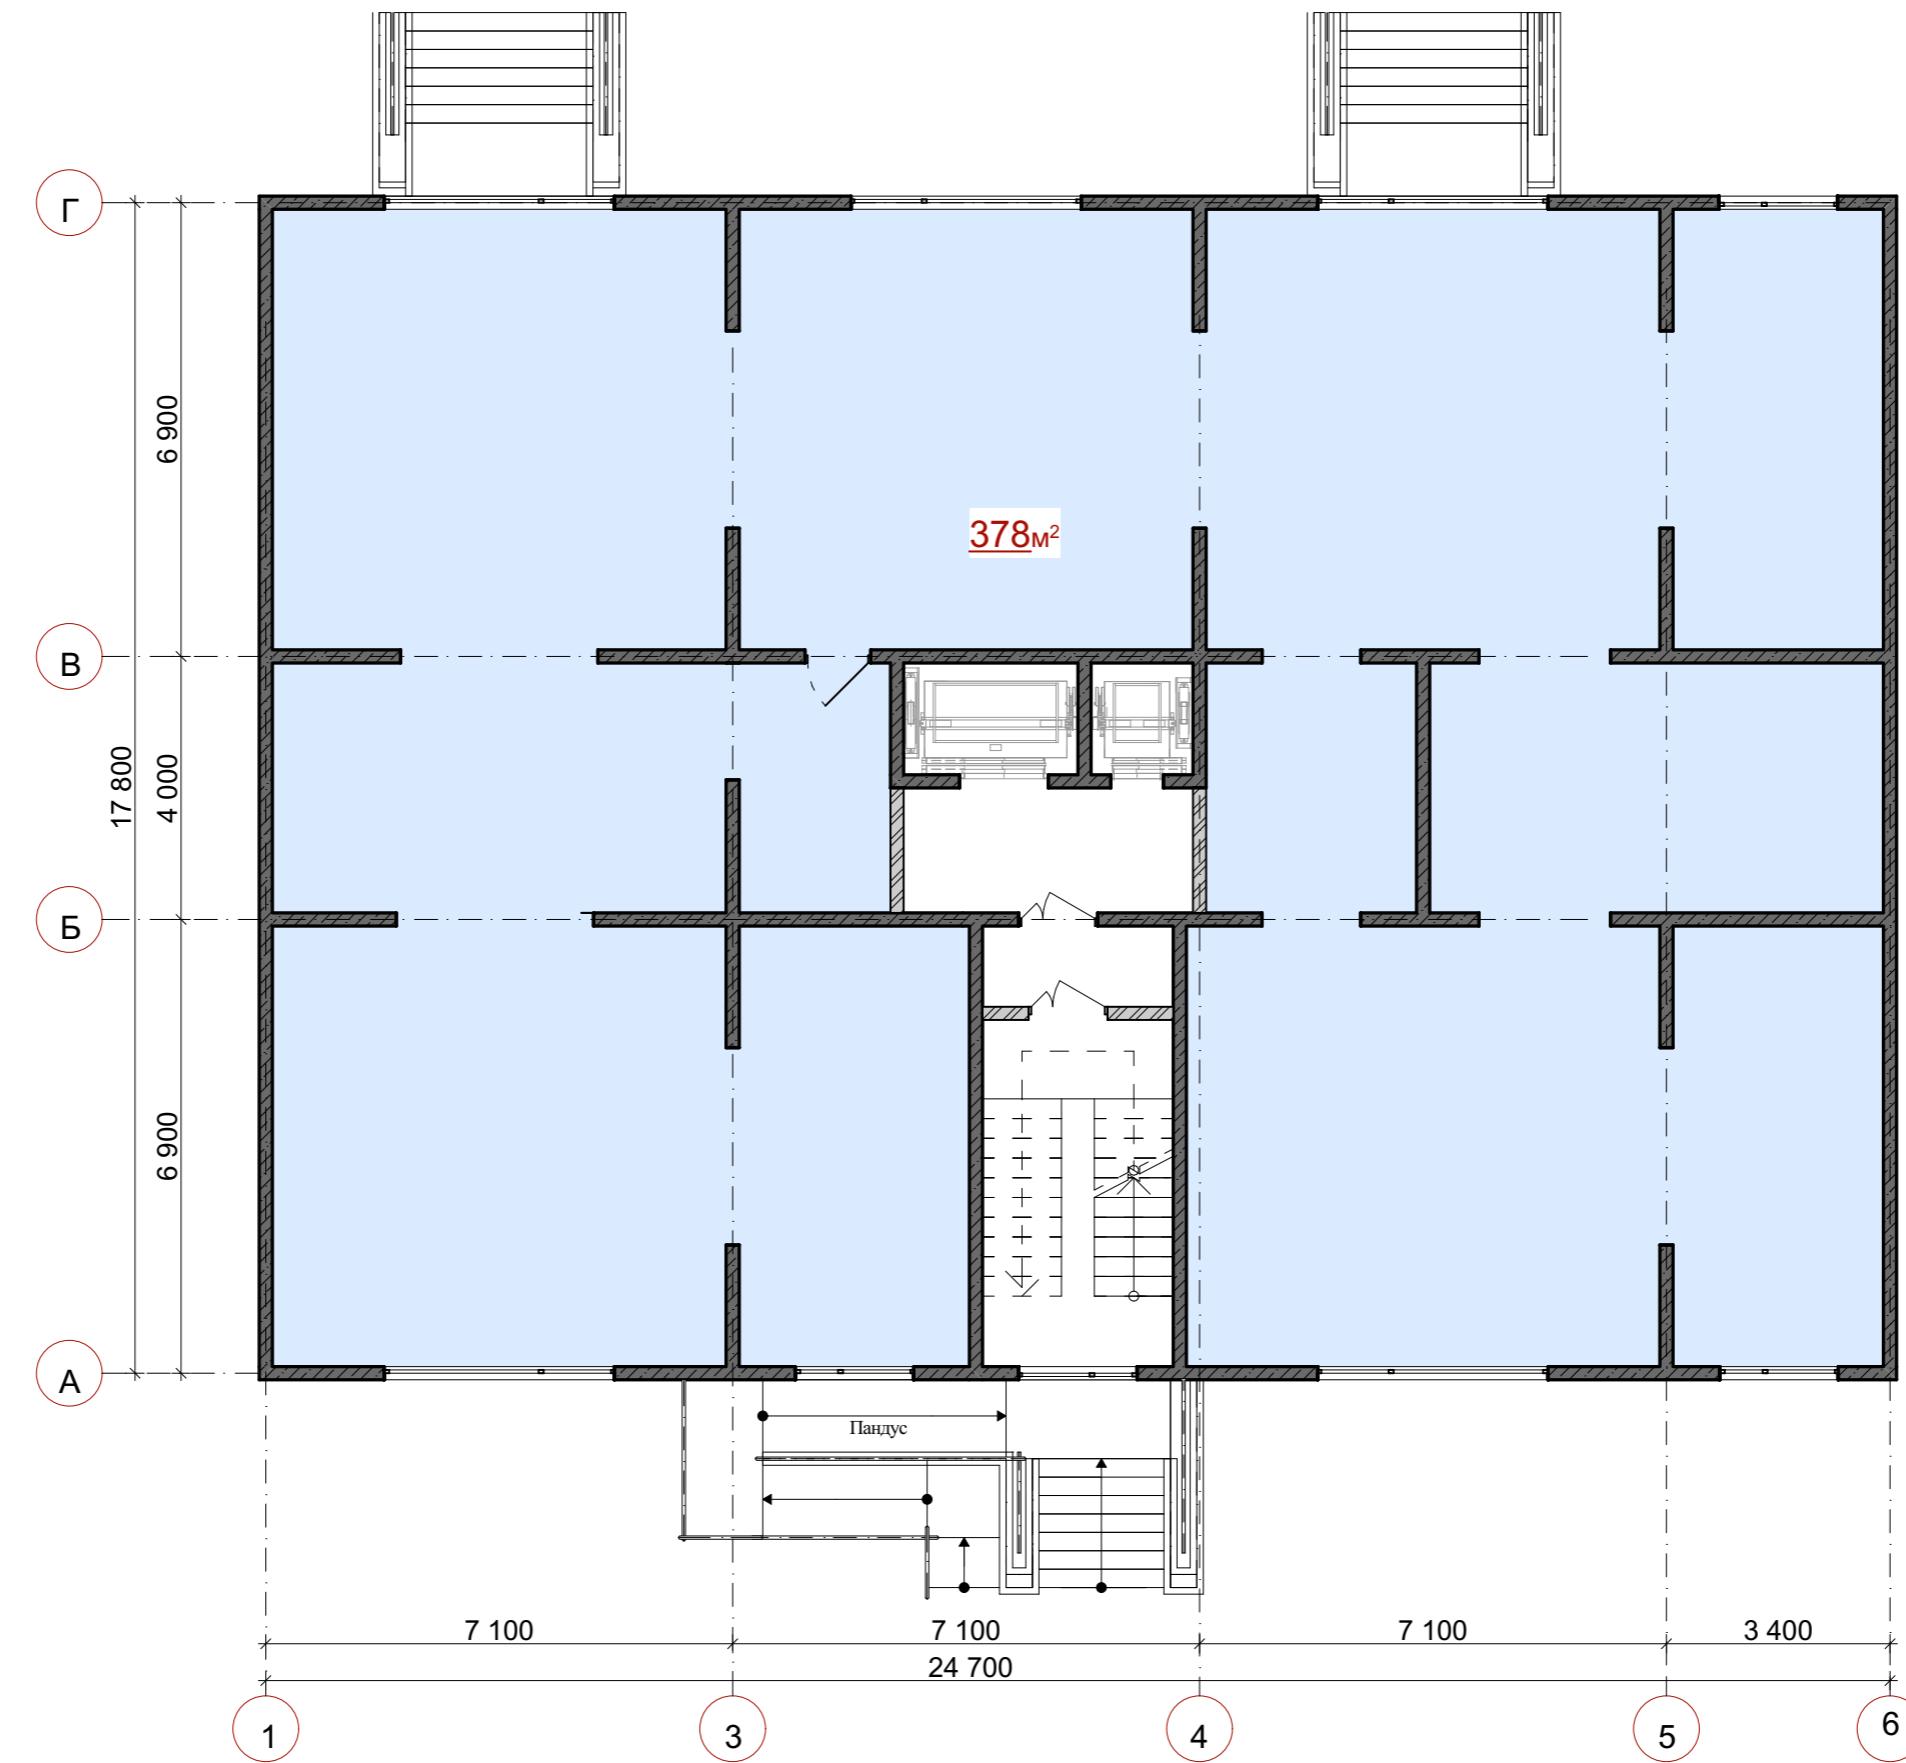

План 2-12 этажа



План 1 го этажа

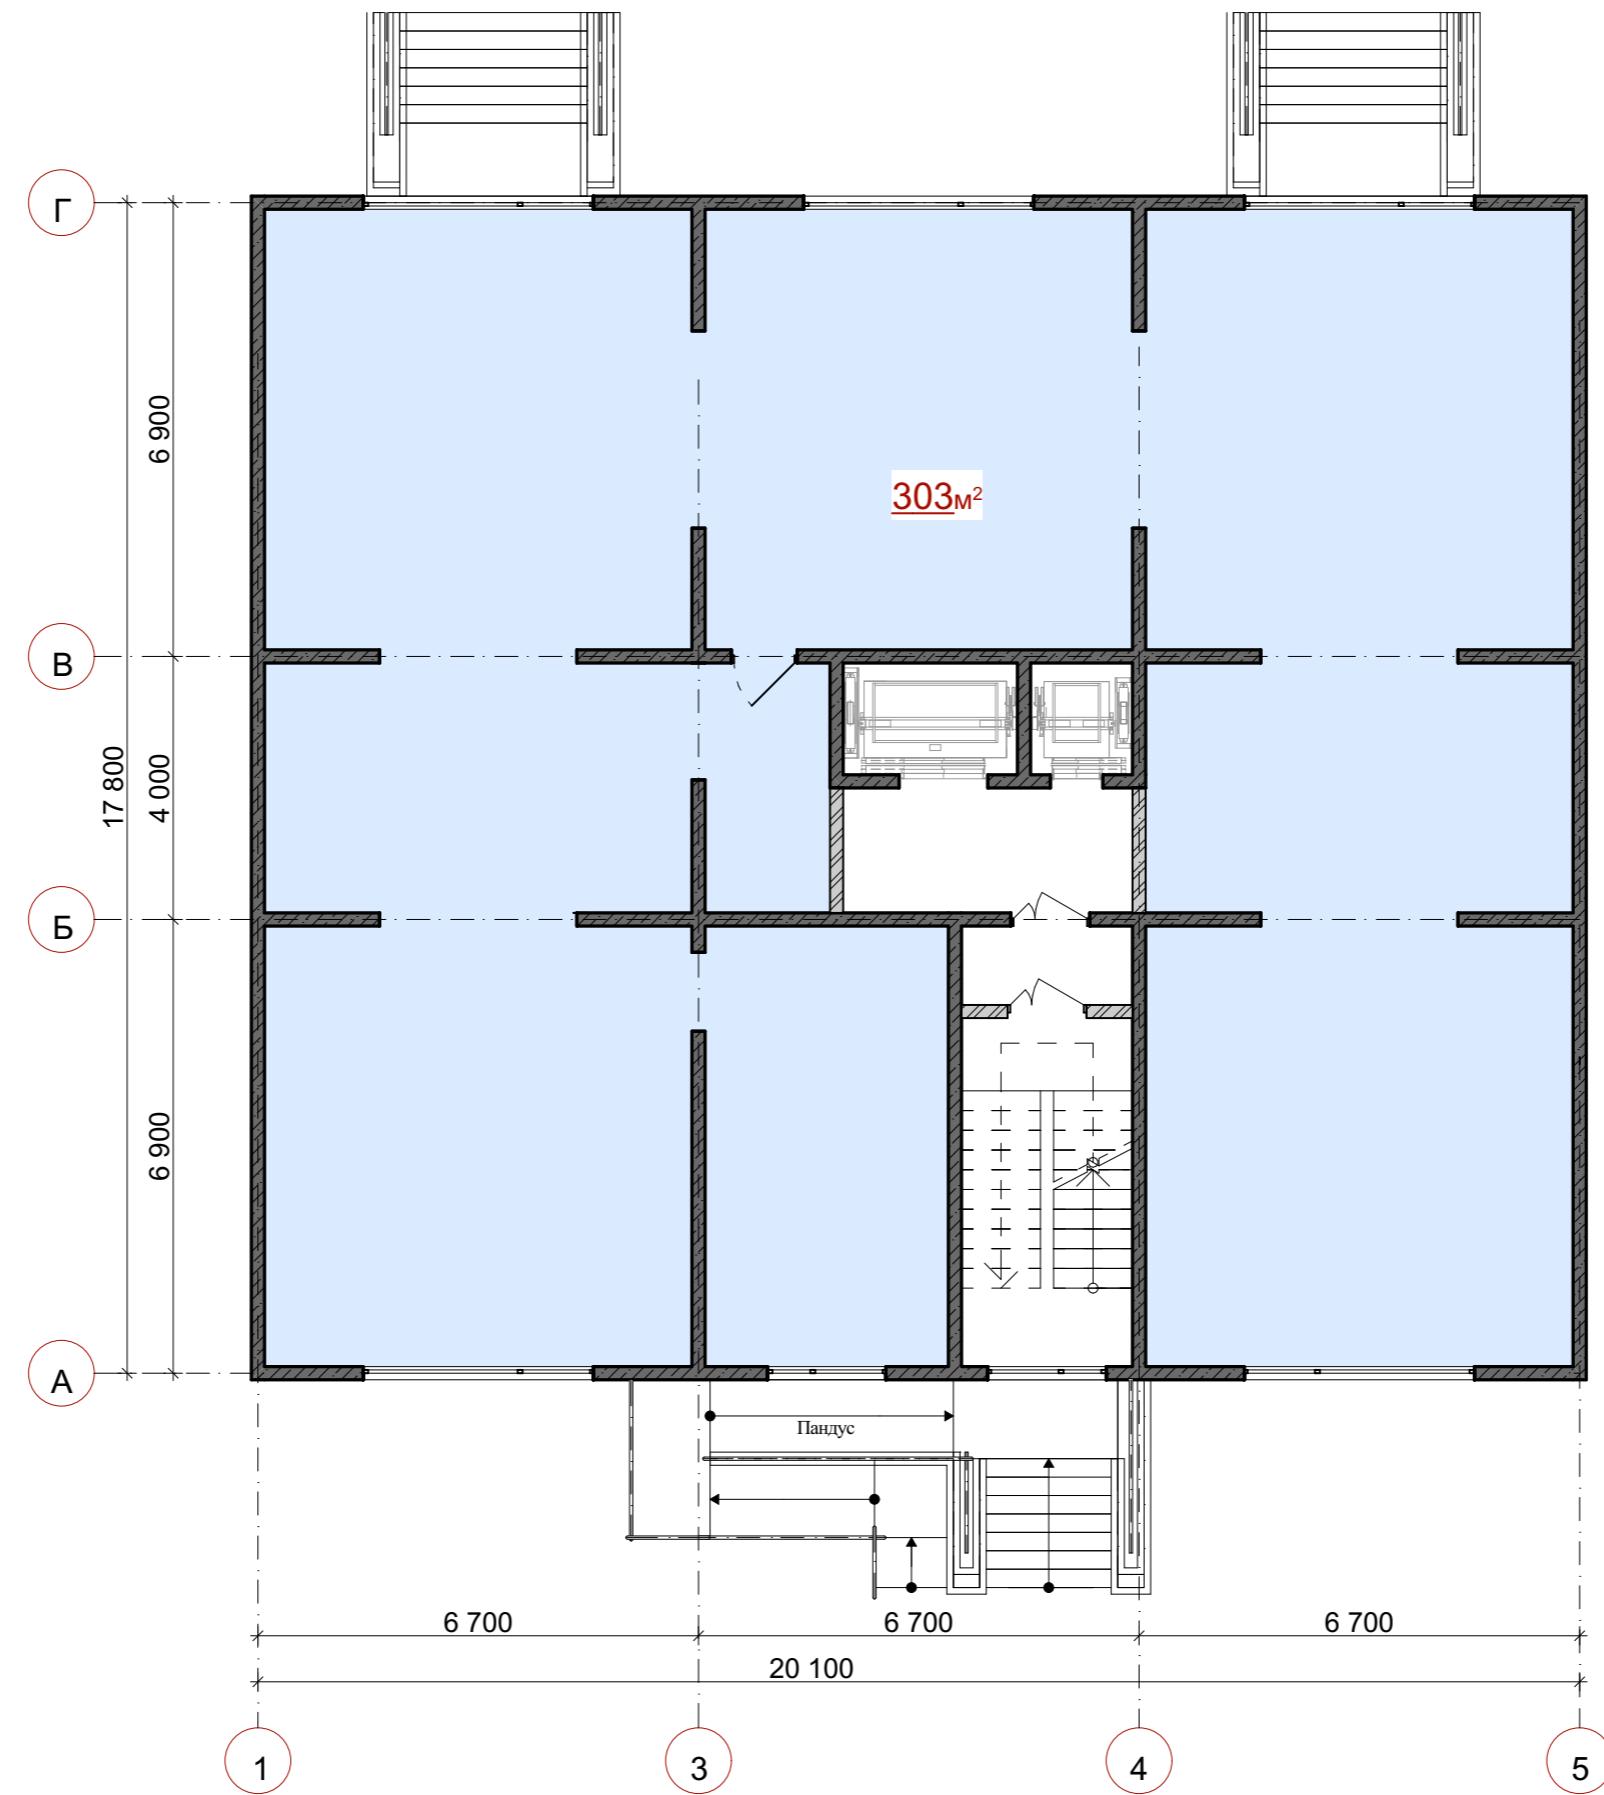

План 2-12 этажа

